PLAN DU REZ-DE-CHAUSSÉE

Échelle 1/50. Cotes en mètres. Épaisseurs : murs extérieurs 0,20, cloisons 0,07.

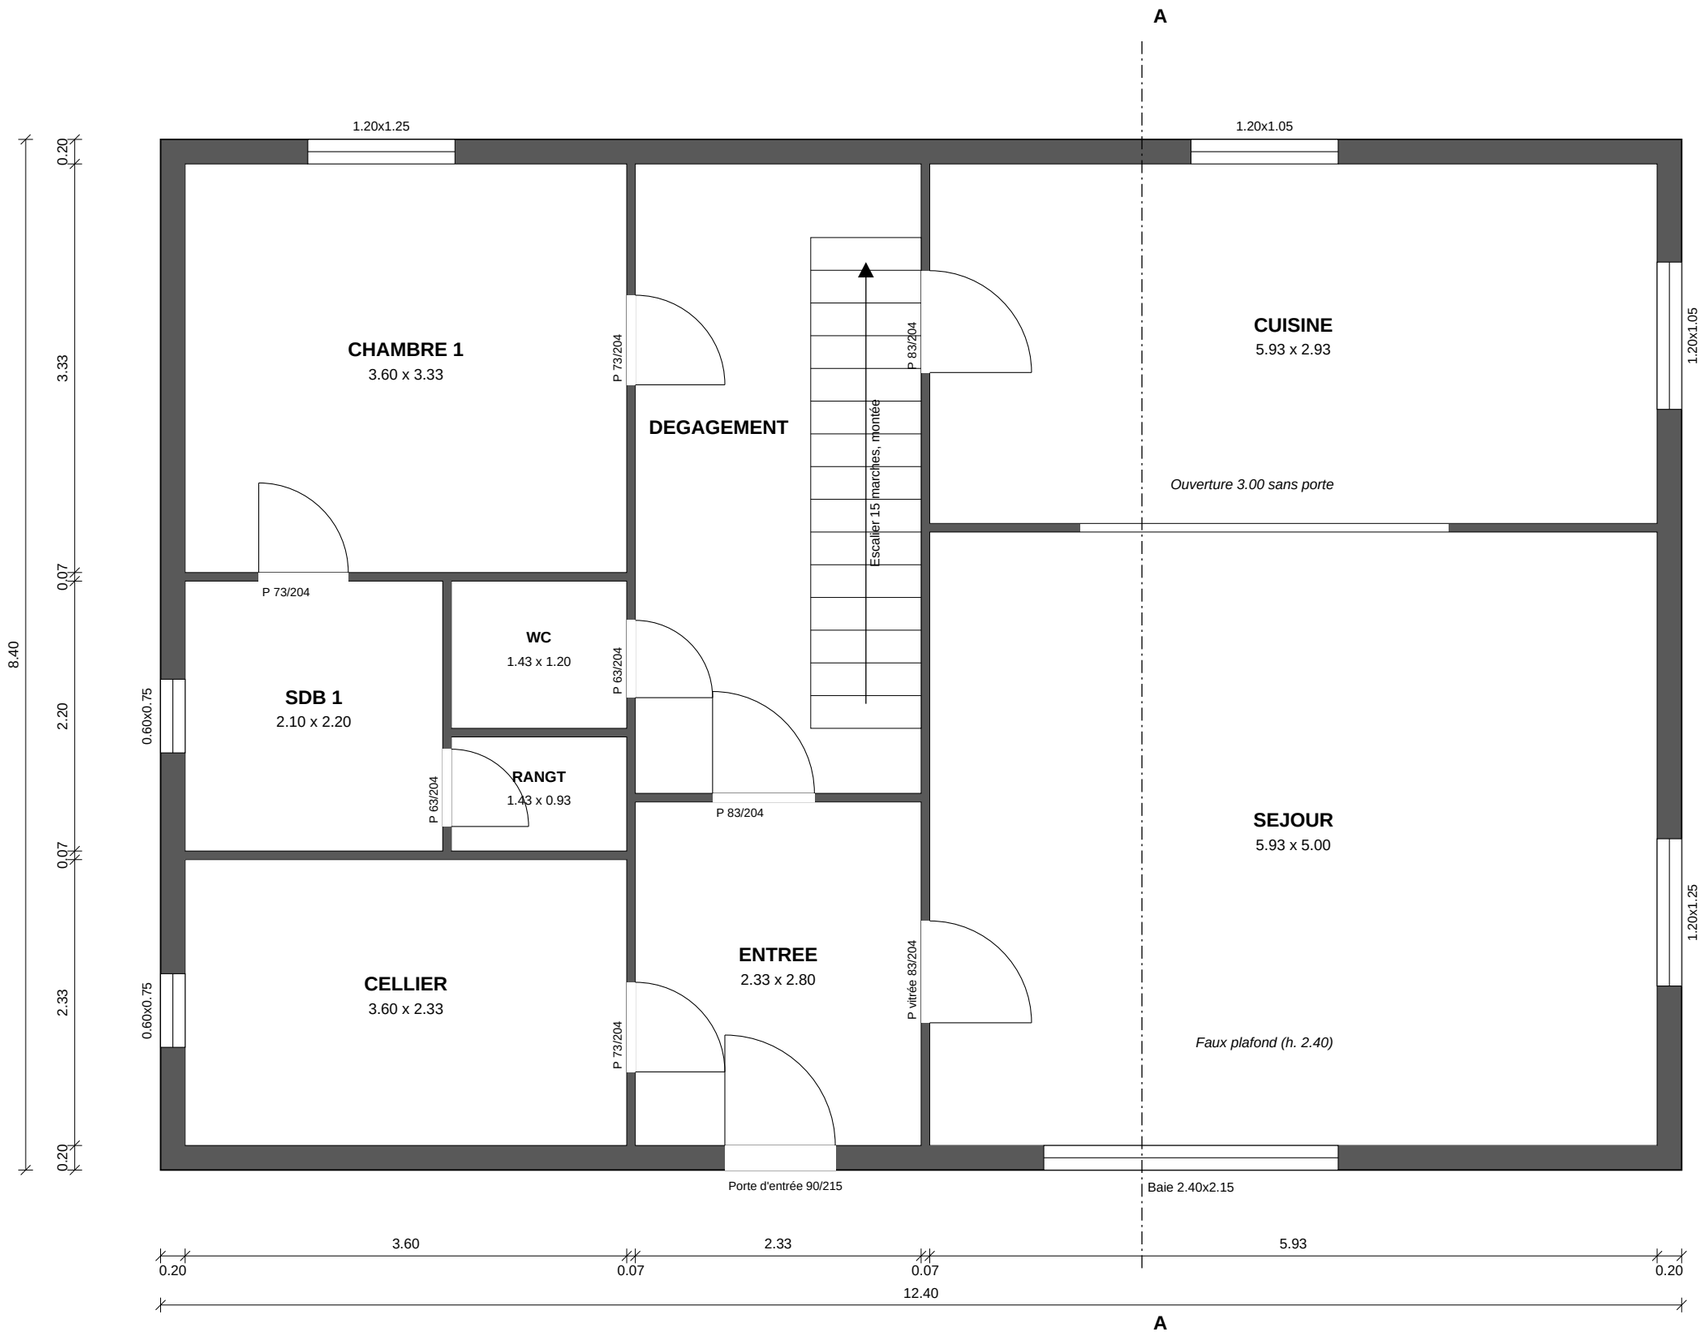

N

Échelle graphique (1/50)

0 m 1 m 2 m 3 m 4 m 5 m

MAISON DES HORTENSIAS

Projet fictif, dessiné pour un exercice de formation

PLAN DU REZ-DE-CHAUSSÉE

Échelle : 1/50ème Format : A3

Hauteurs : voir coupe A-A

Date : 12/11/2026 Indice A

Données fictives, libres de réutilisation en formation. Supports lumiere-ia.com